

Mr. Manoker – Gf Bedroom

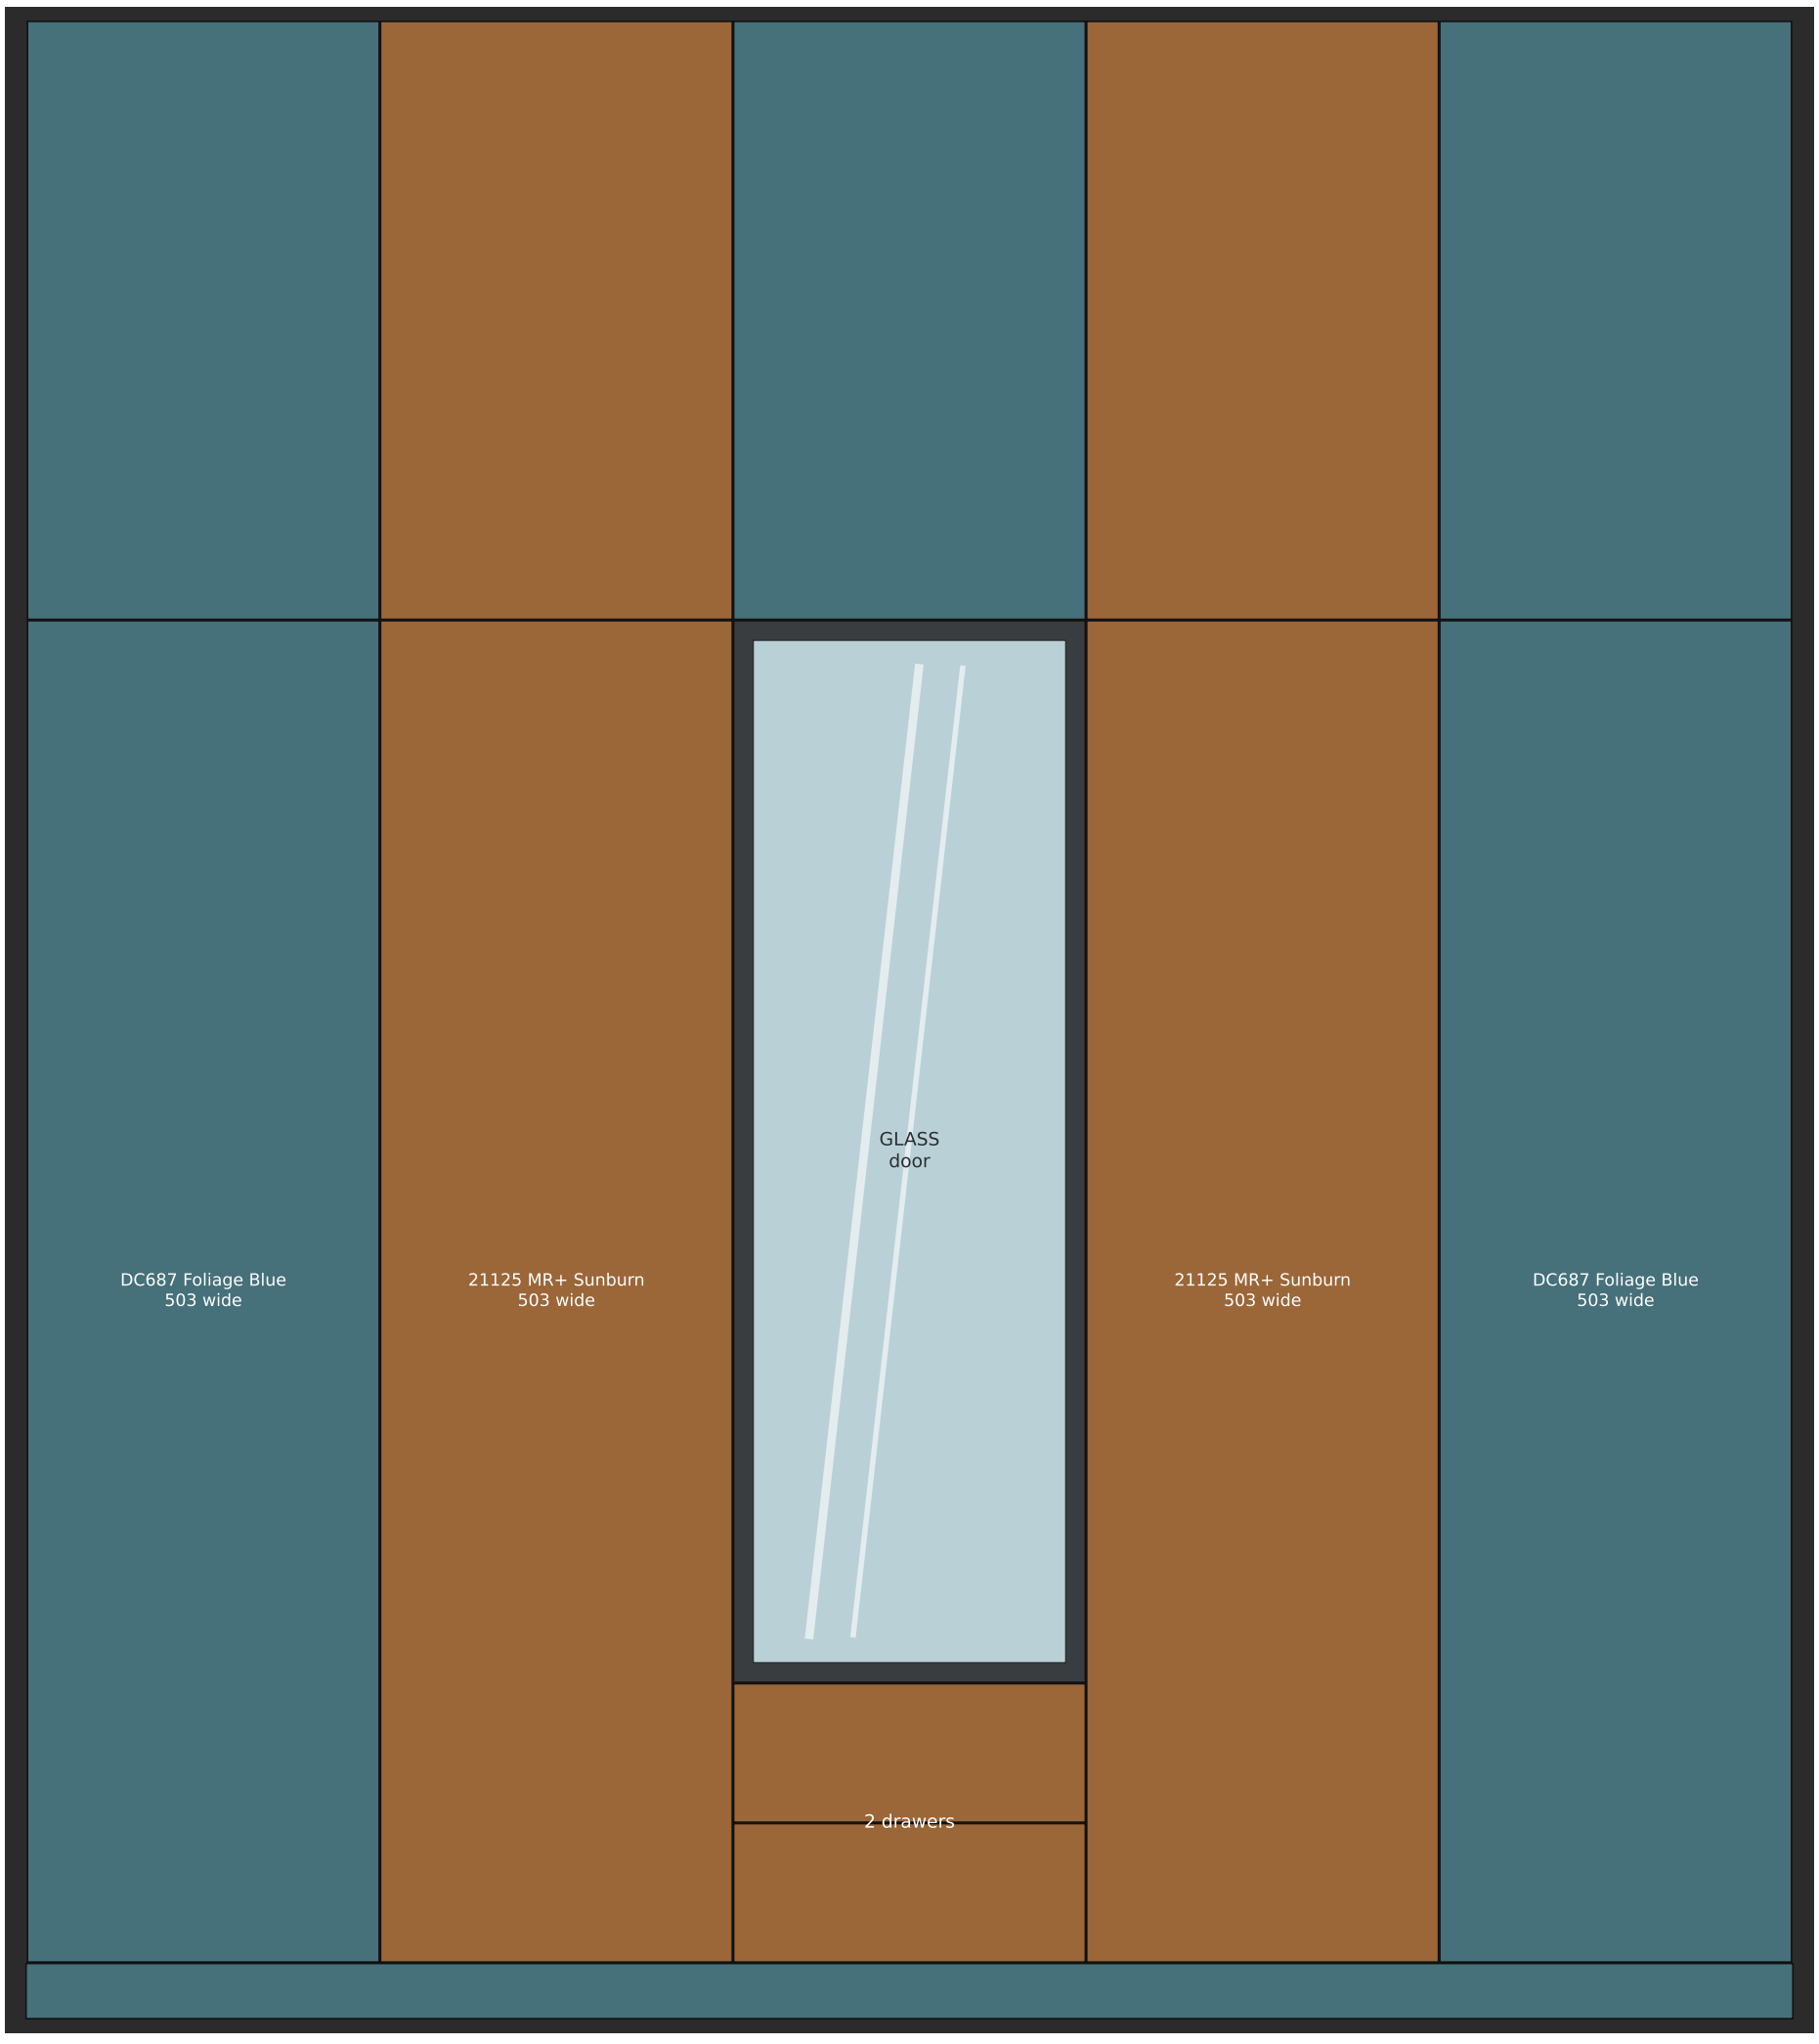

GF BEDROOM

5 doors (centre glass) + 5 loft doors · door 503 wide · DC687 Foliage Blue (Advance) + 21125 MR+ Sunburn (Merino)


Mr. Manoker – 1St Floor M.Bedroom

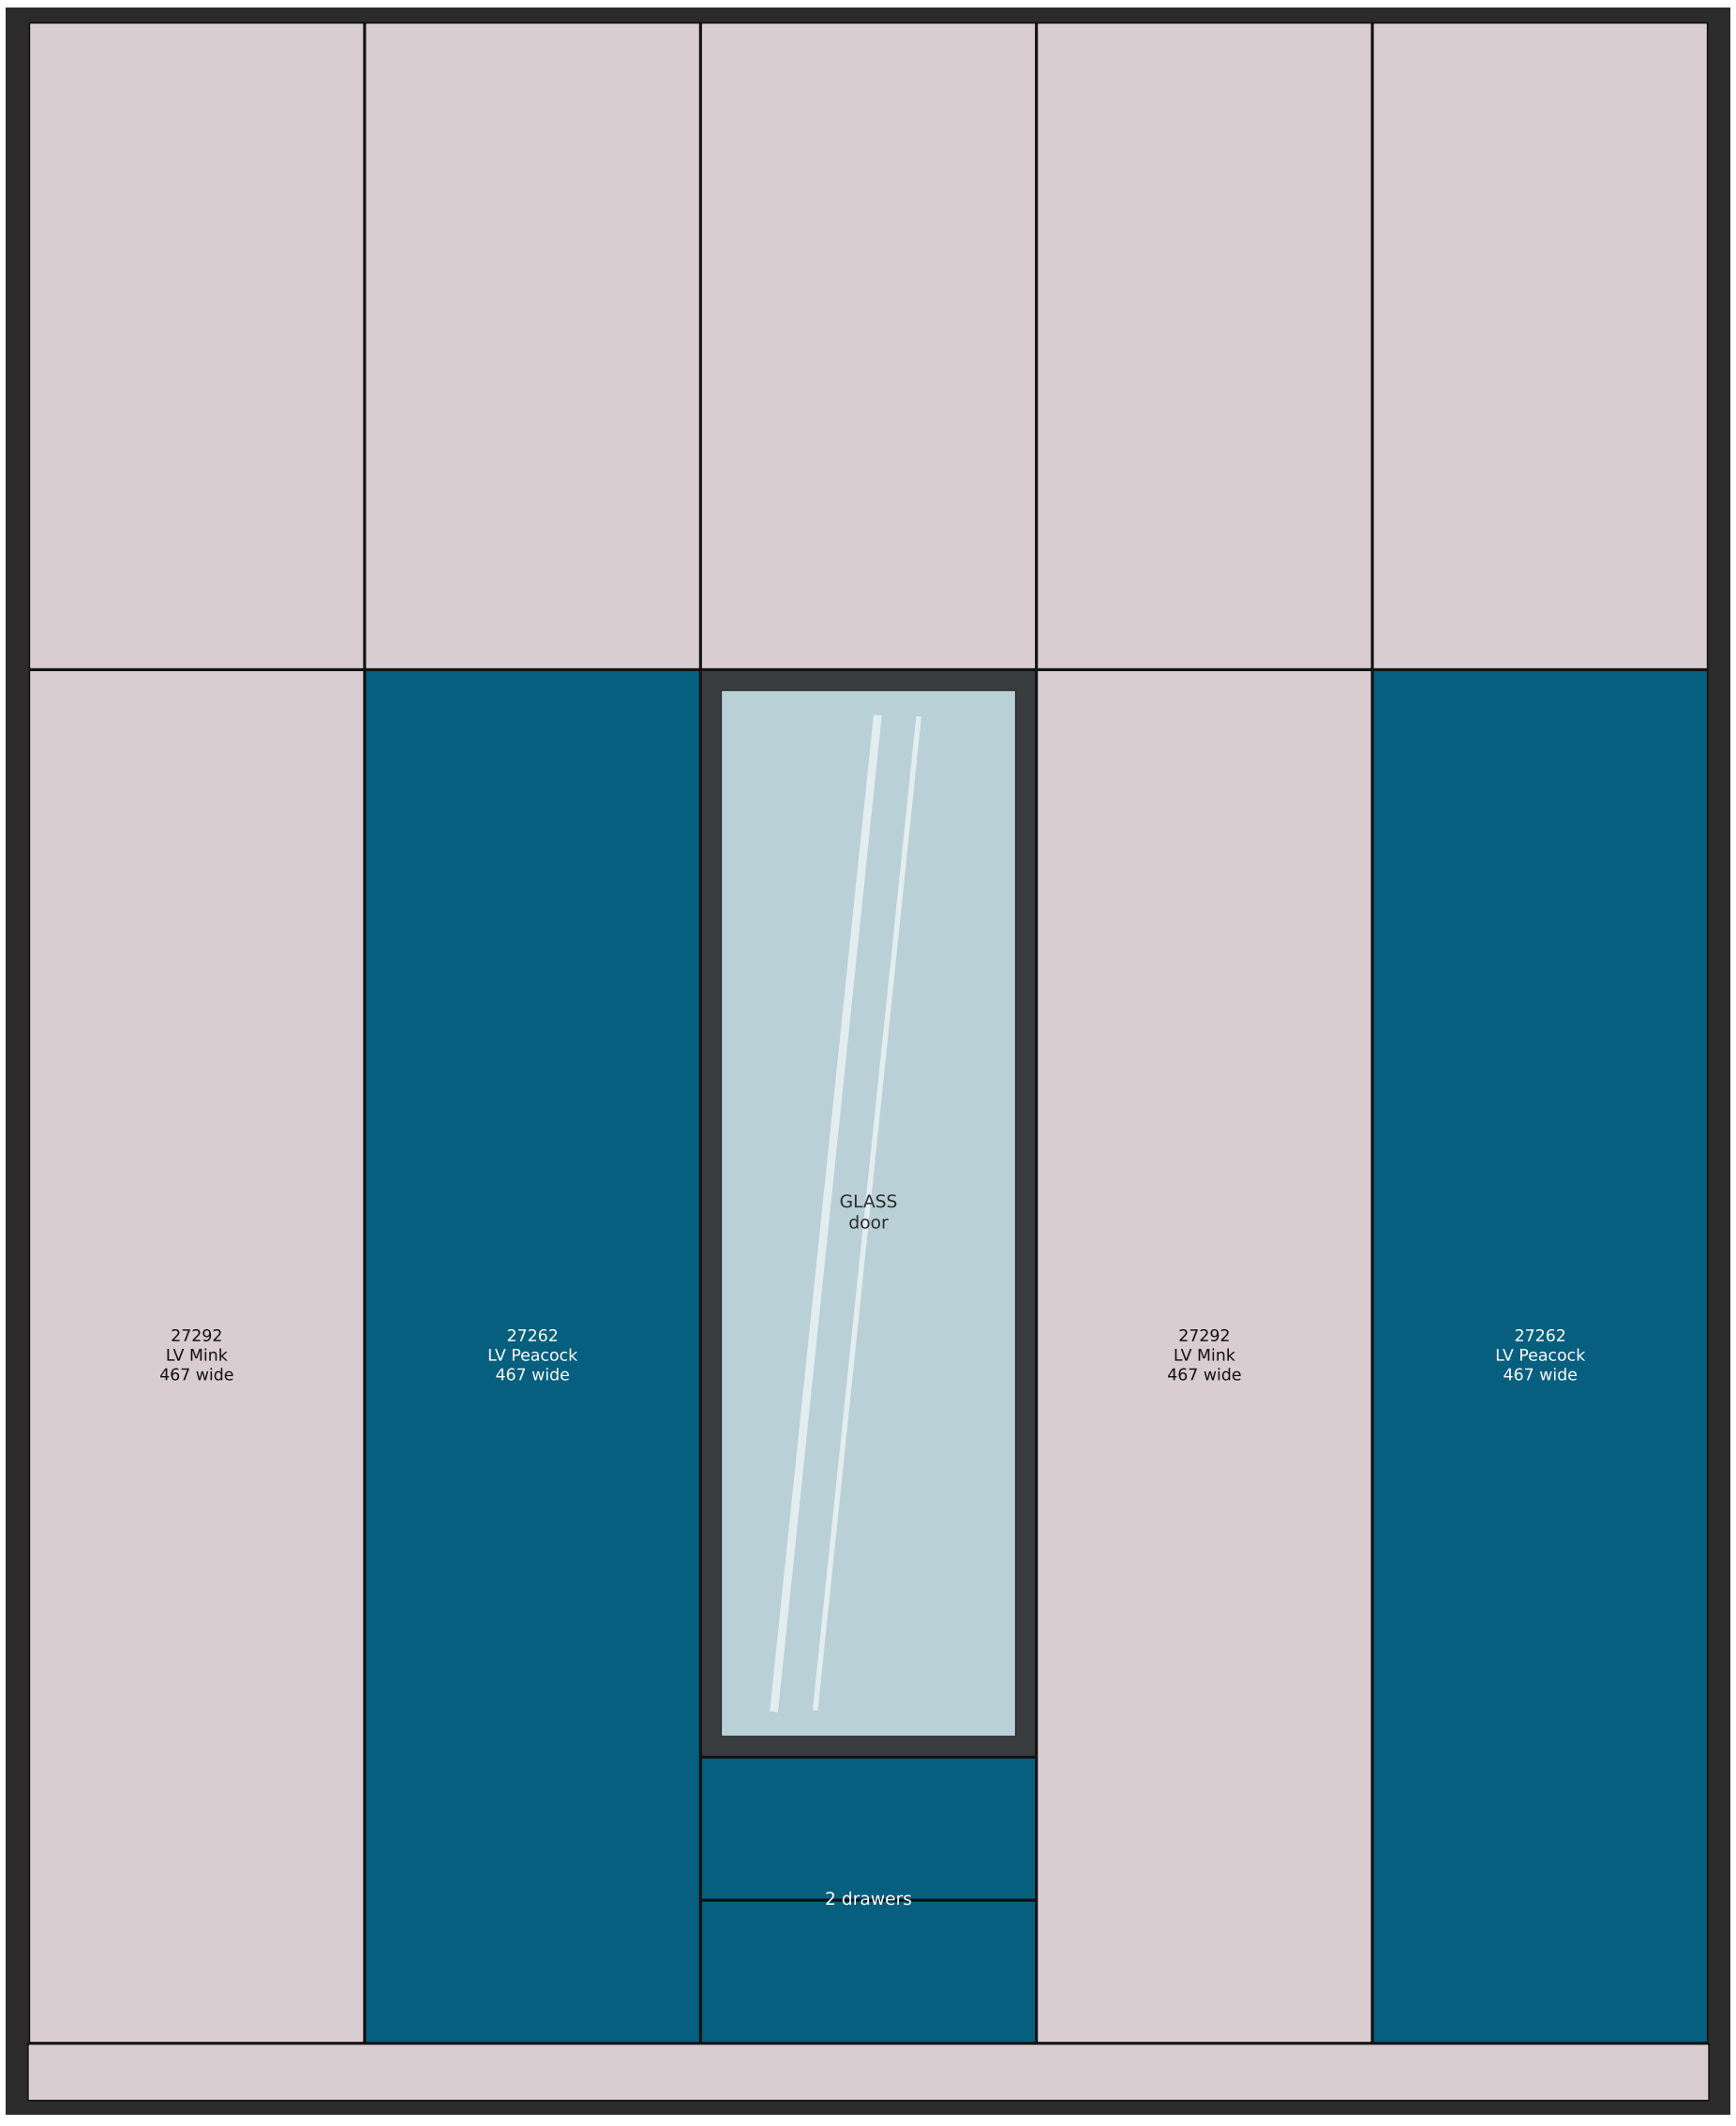

1ST FLOOR M.BEDROOM

5 doors (centre glass) + 5 loft doors · door 467 wide · 27292 LV Mink + 27262 LV Peacock


Mr. Manoker – 1St Floor Bedroom 2

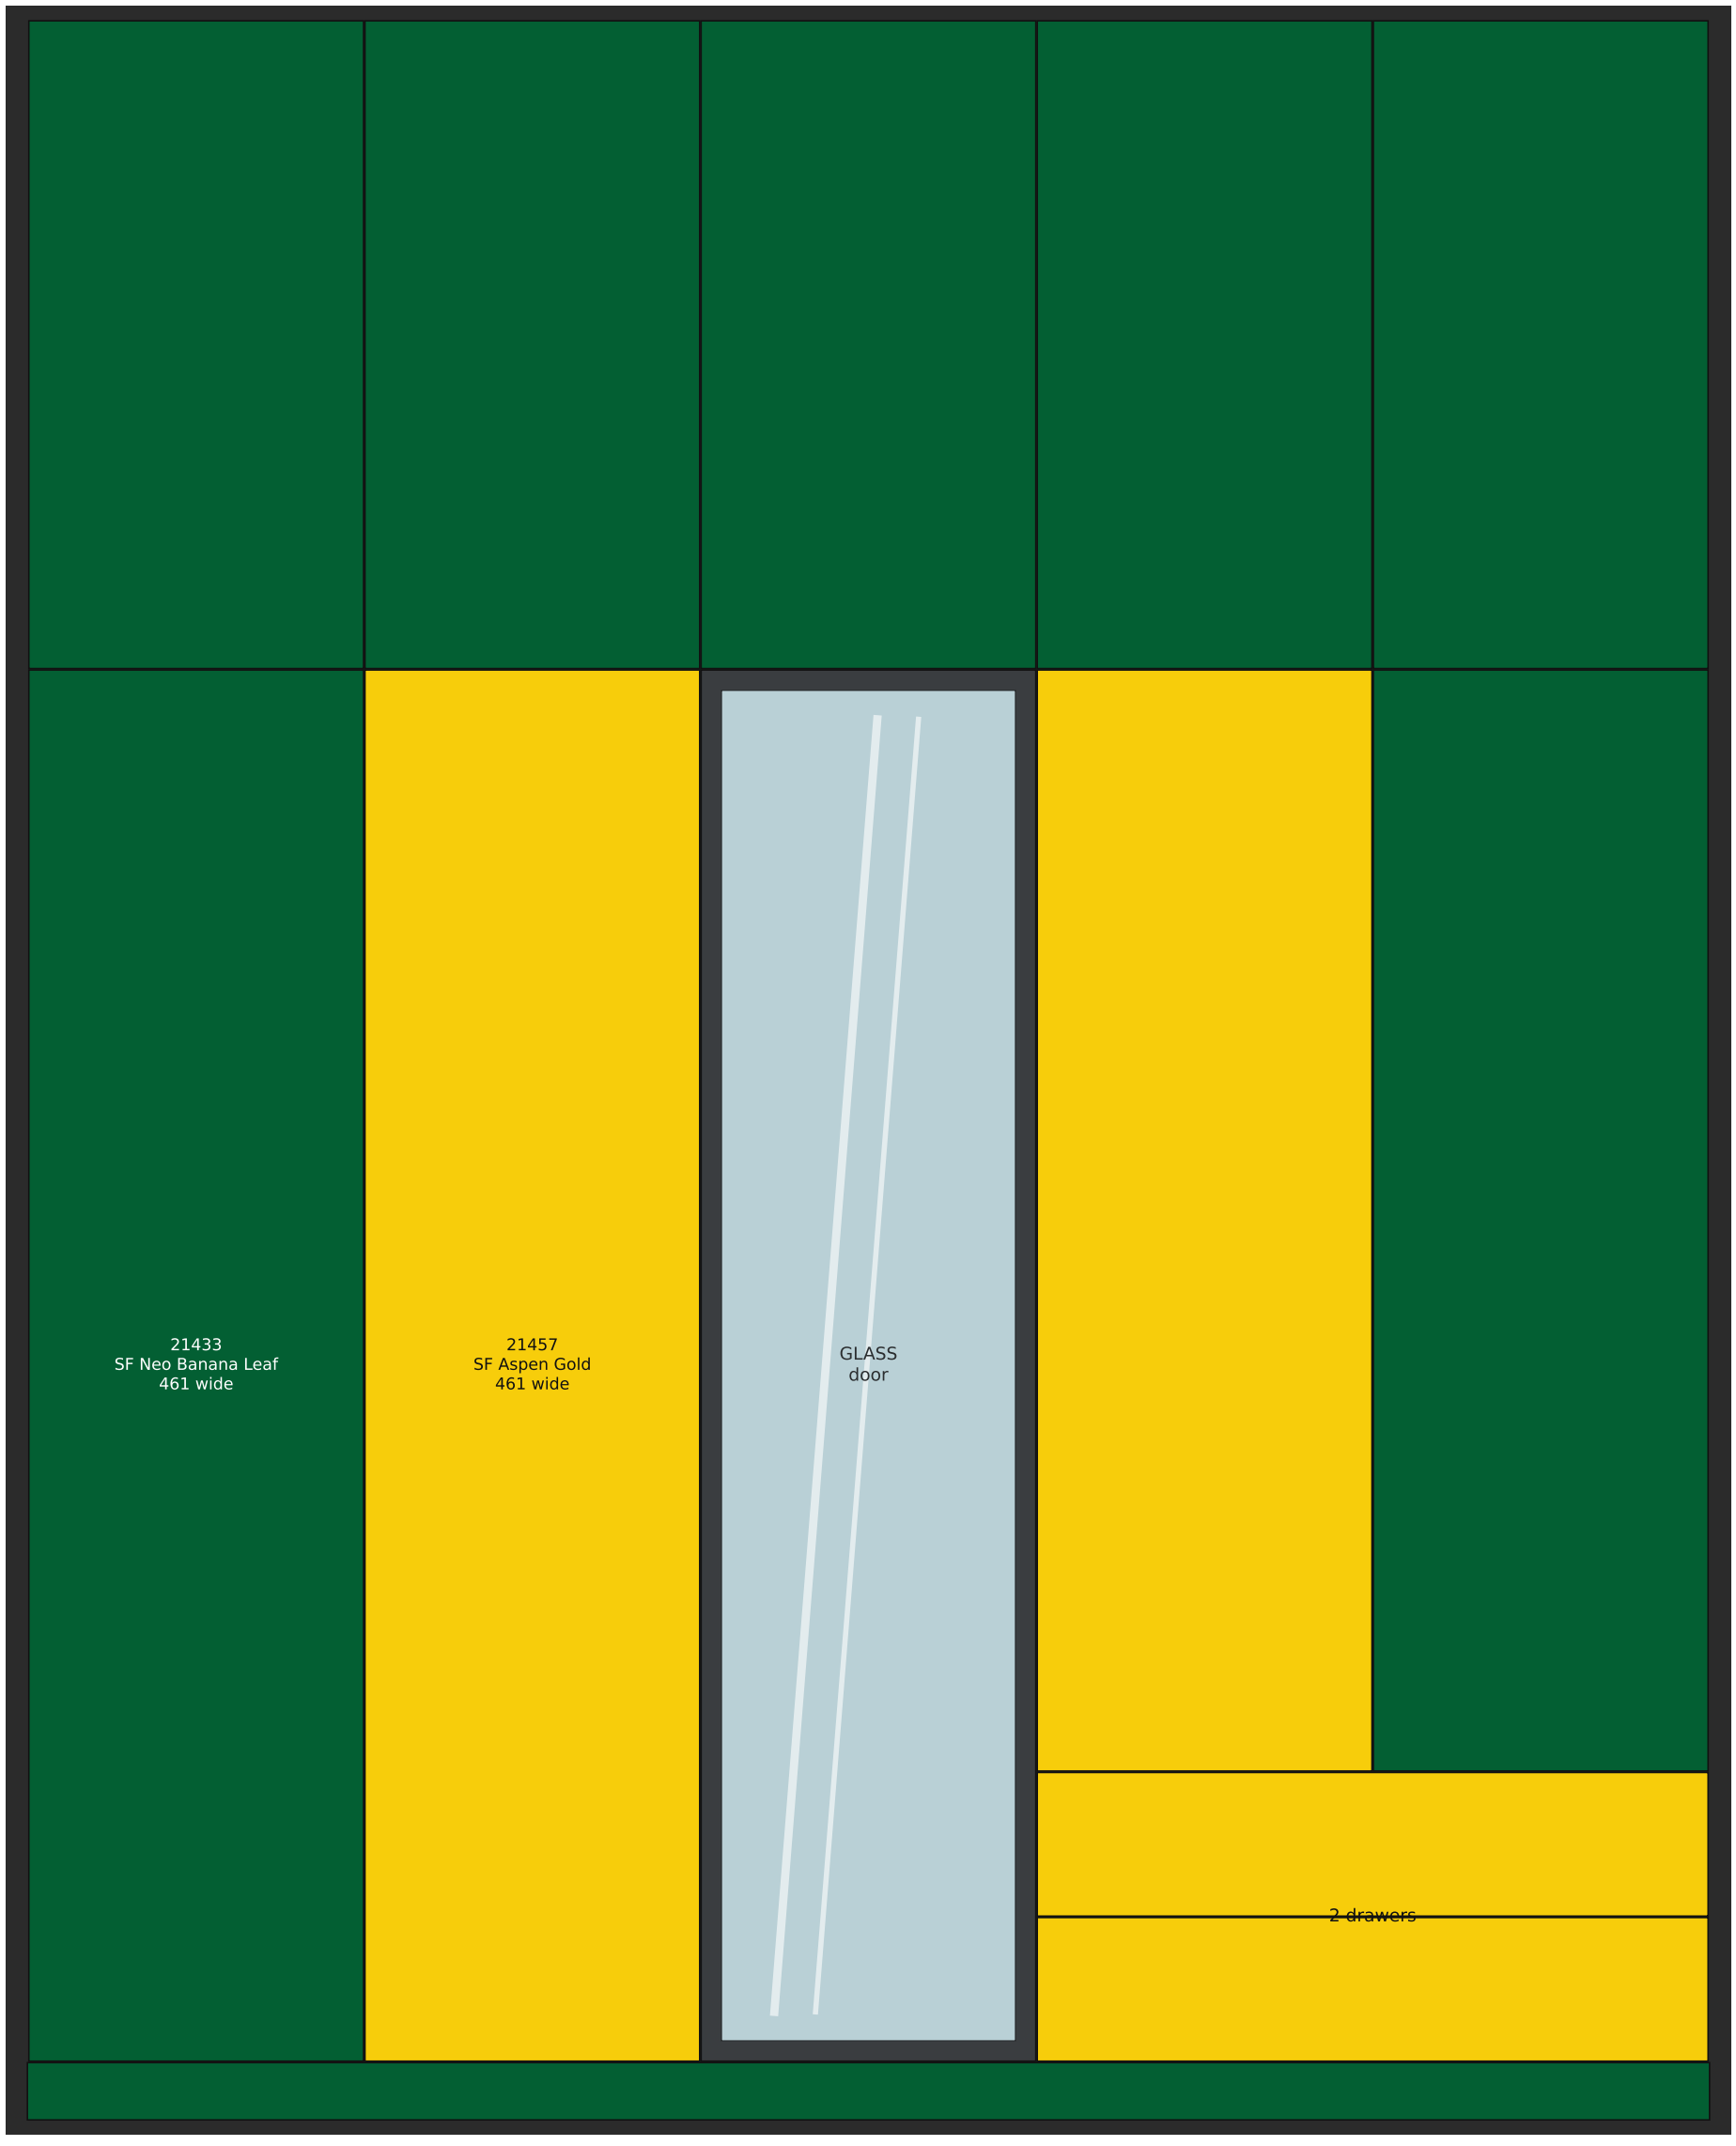

1ST FLOOR BEDROOM 2

5 doors (centre glass) + 5 loft doors · door 461 wide · 21433 SF Neo Banana Leaf + 21457 SF Aspen Gold

Mr. Manoker – 2Nd Floor Bedroom

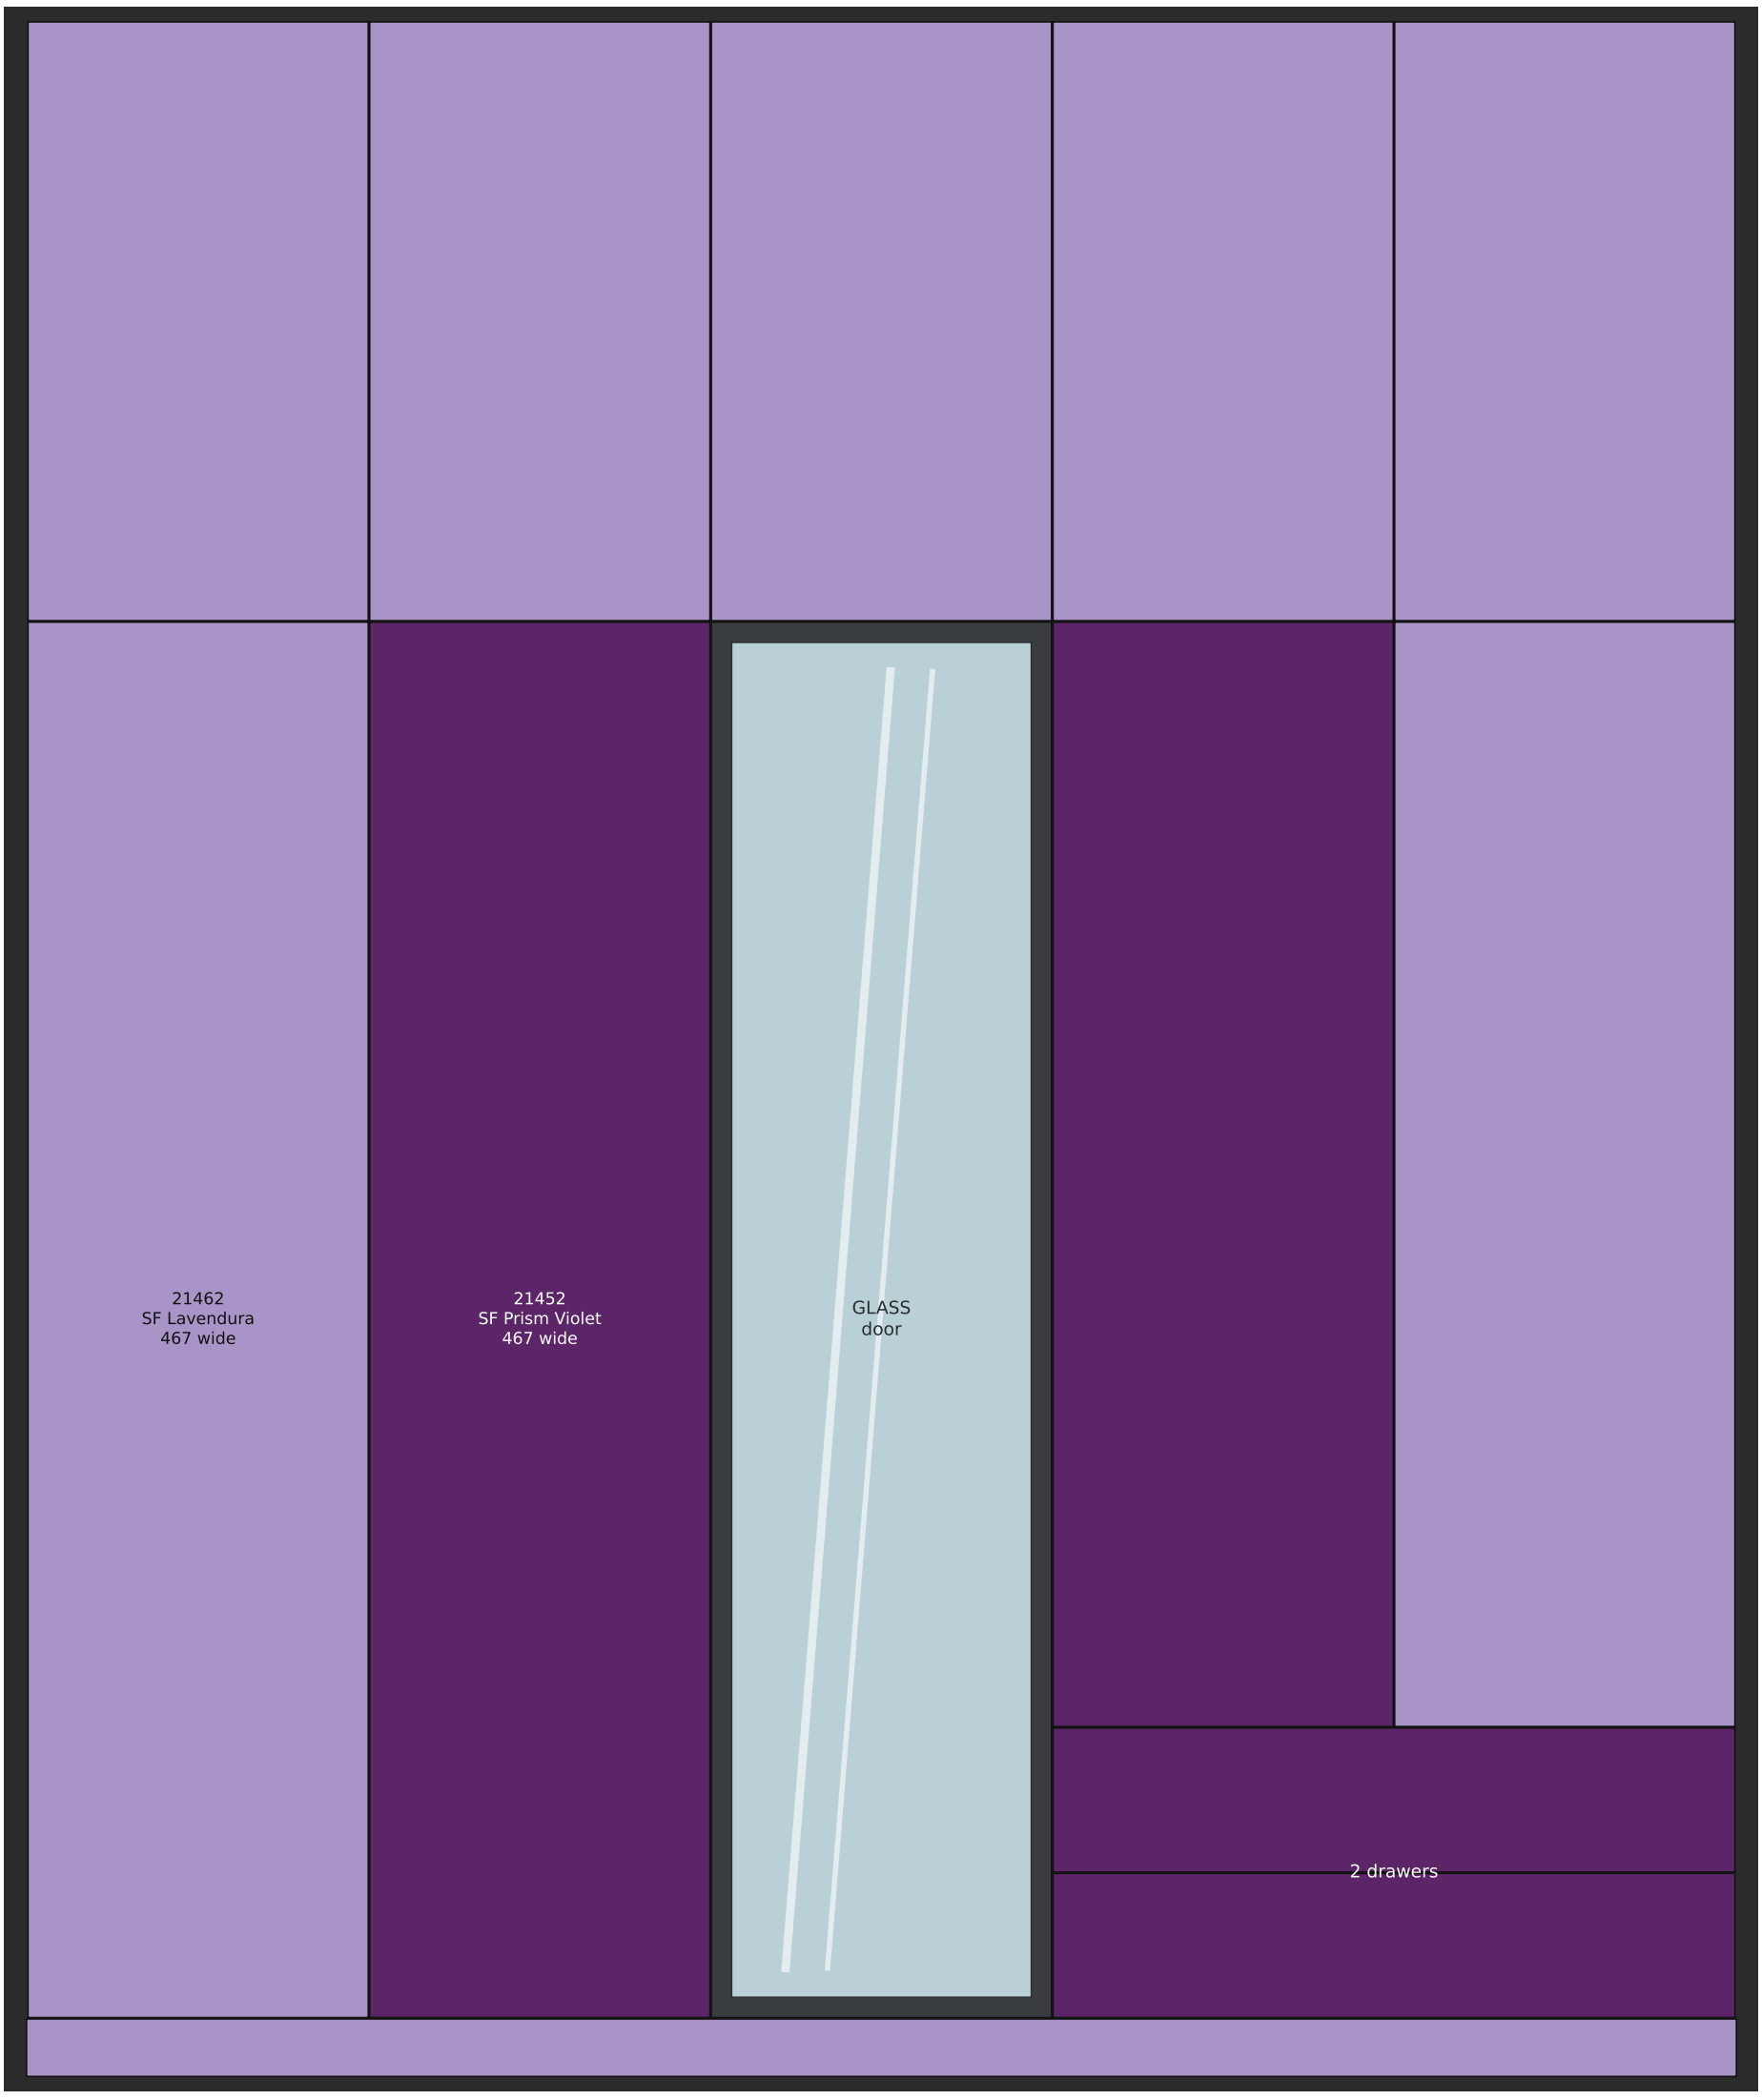

2ND FLOOR BEDROOM

5 doors (centre glass) + 5 loft doors · door 467 wide · 21462 SF Lavendura + 21452 SF Prism Violet

Mr. Manoker – Kitchen (view 1)



Top: 676 Aqua Green · Bottom: 626 DG Dream Green (Advance)

Mr. Manoker – Kitchen (view 2)



Top: 676 Aqua Green · Bottom: 626 DG Dream Green (Advance)